

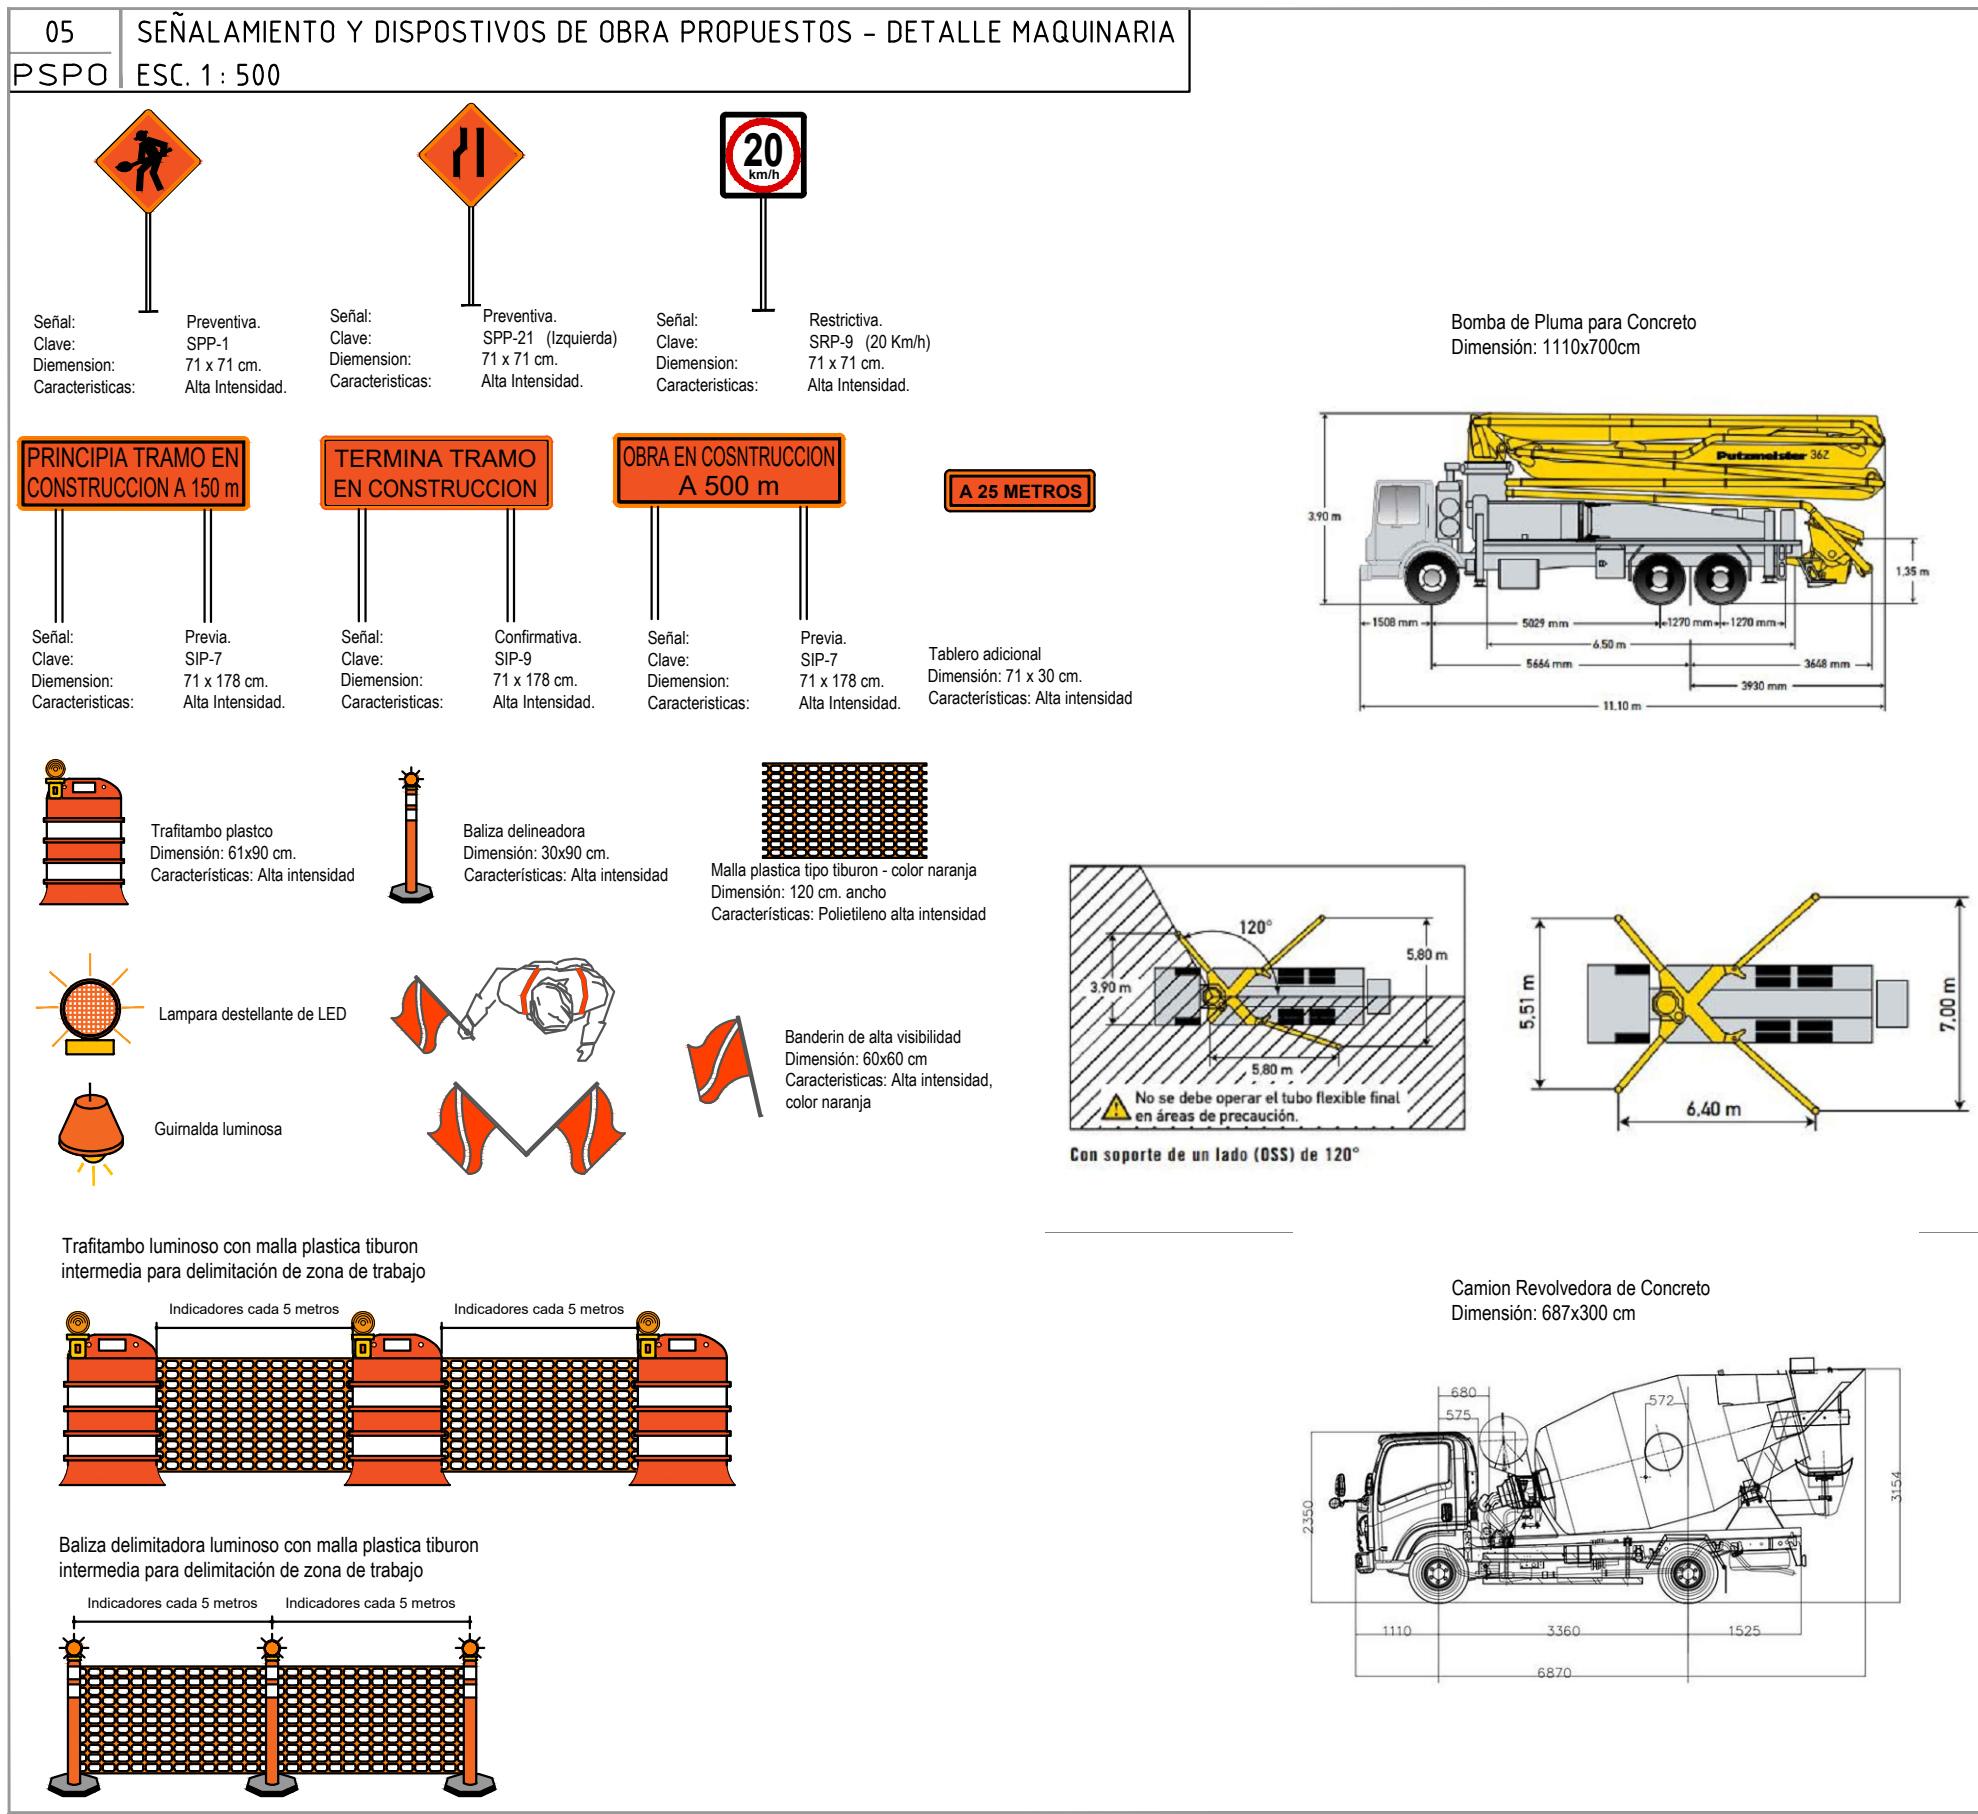
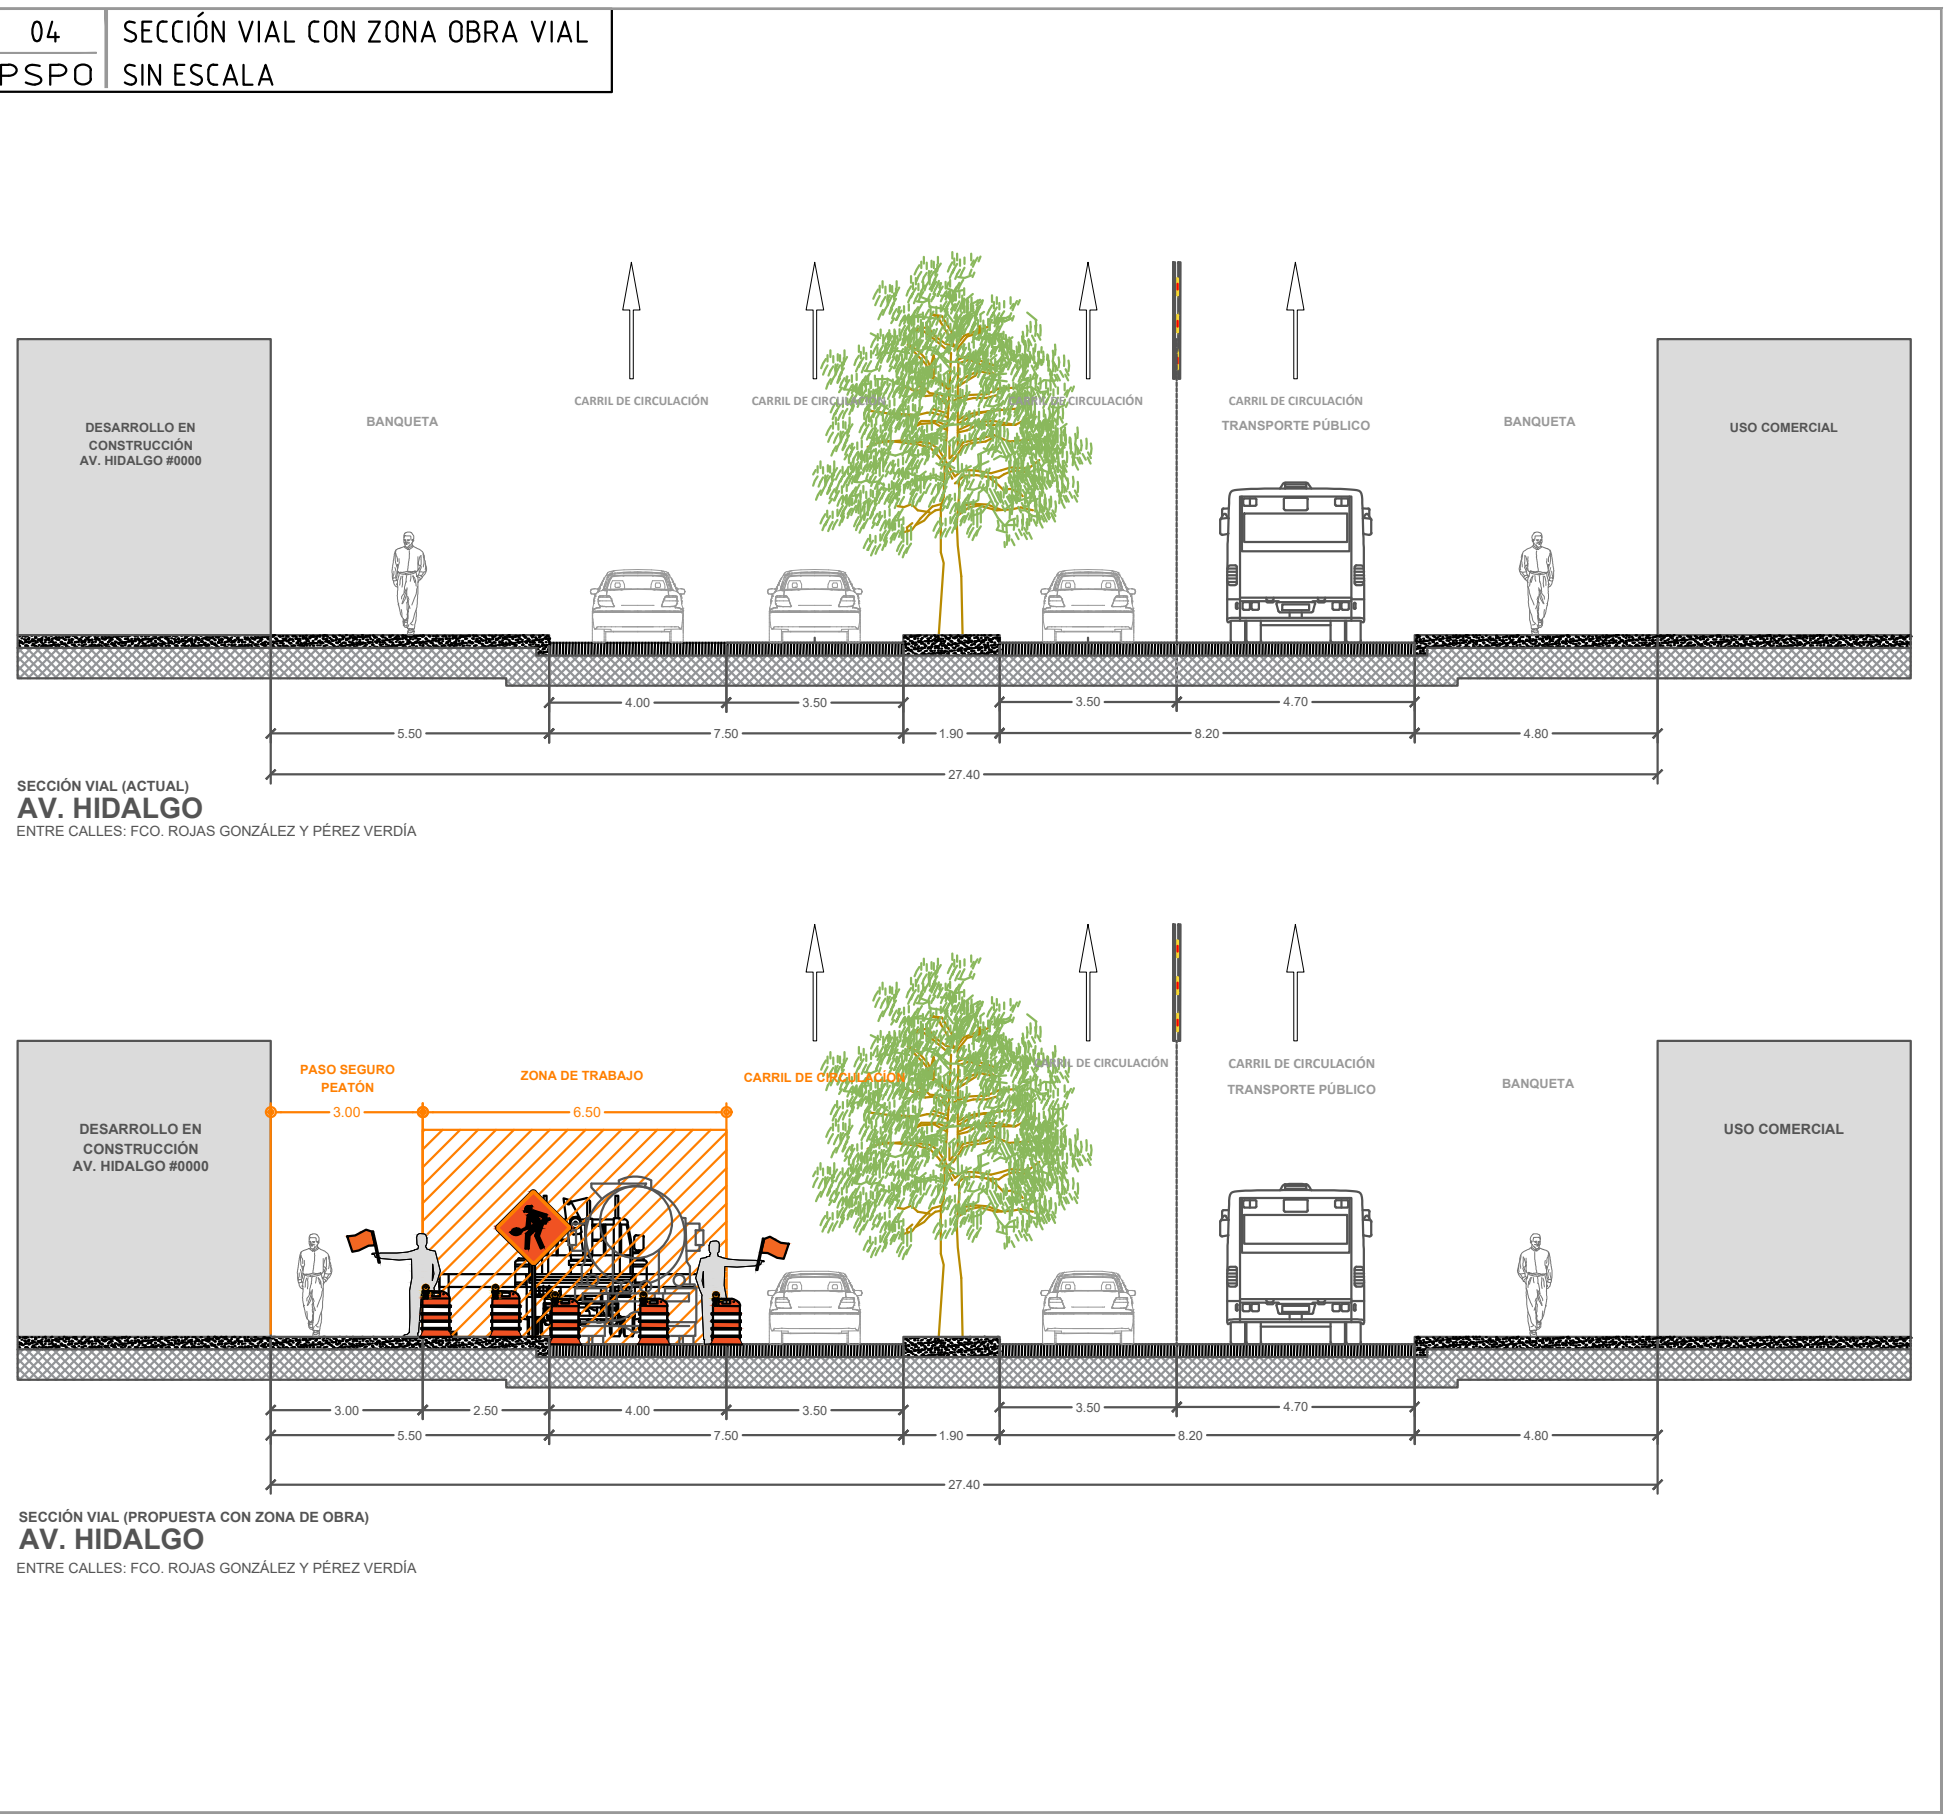
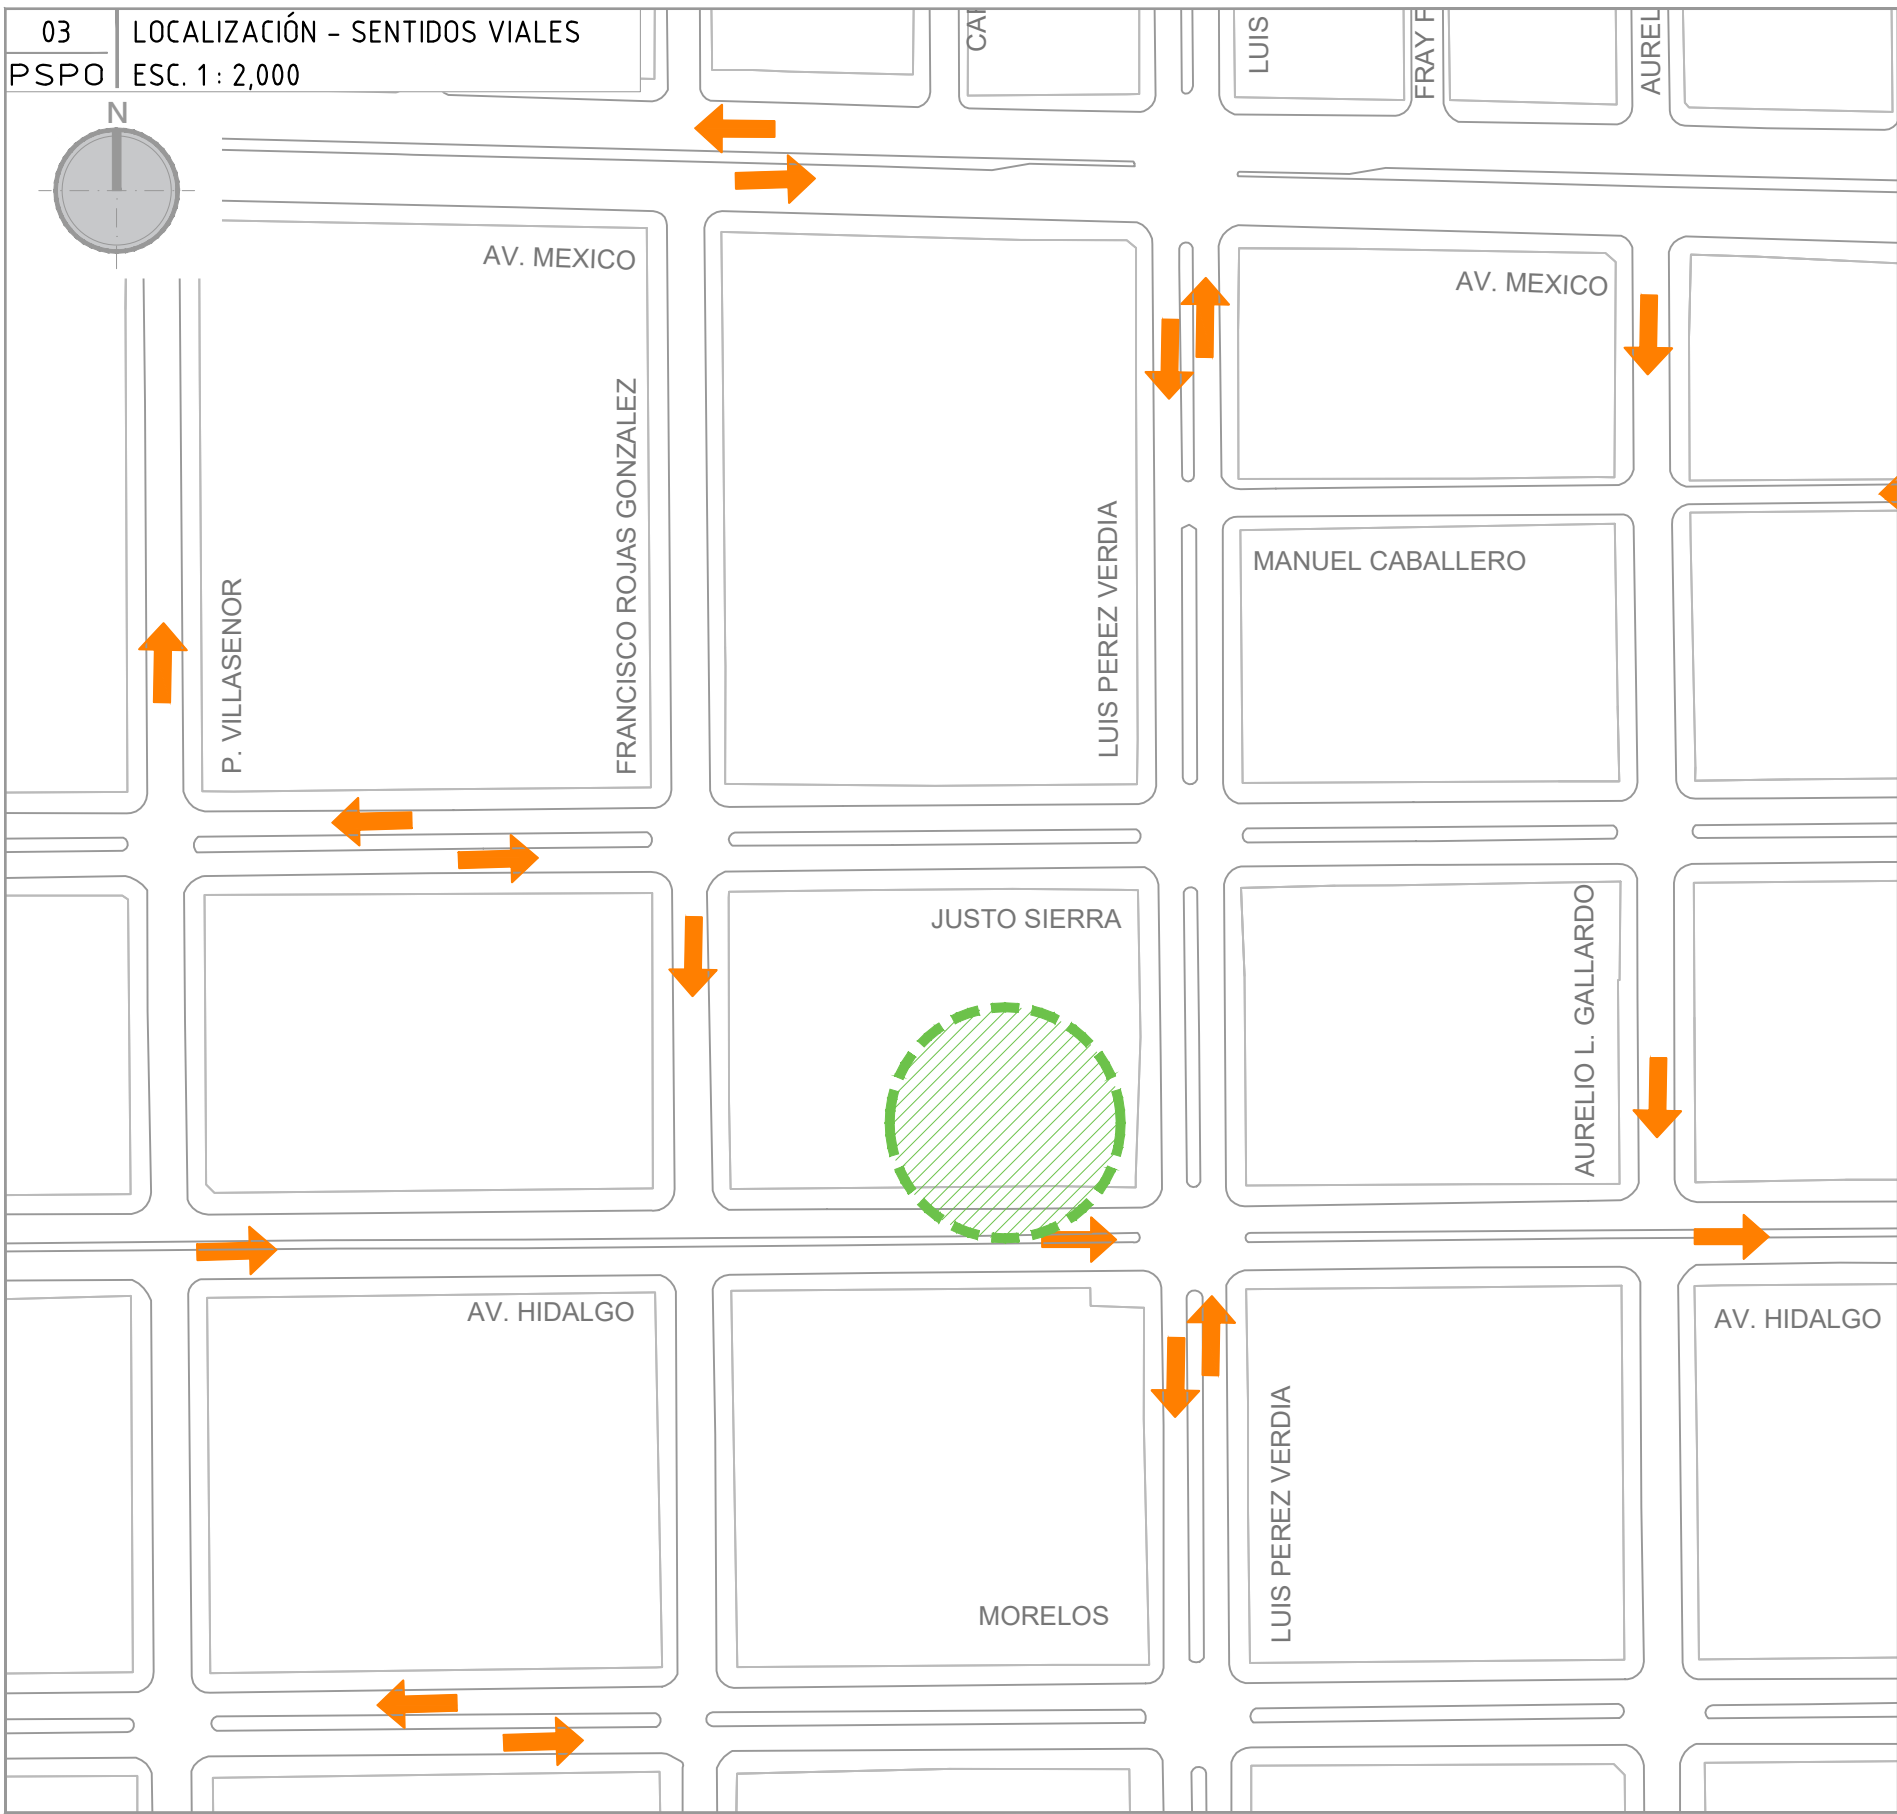


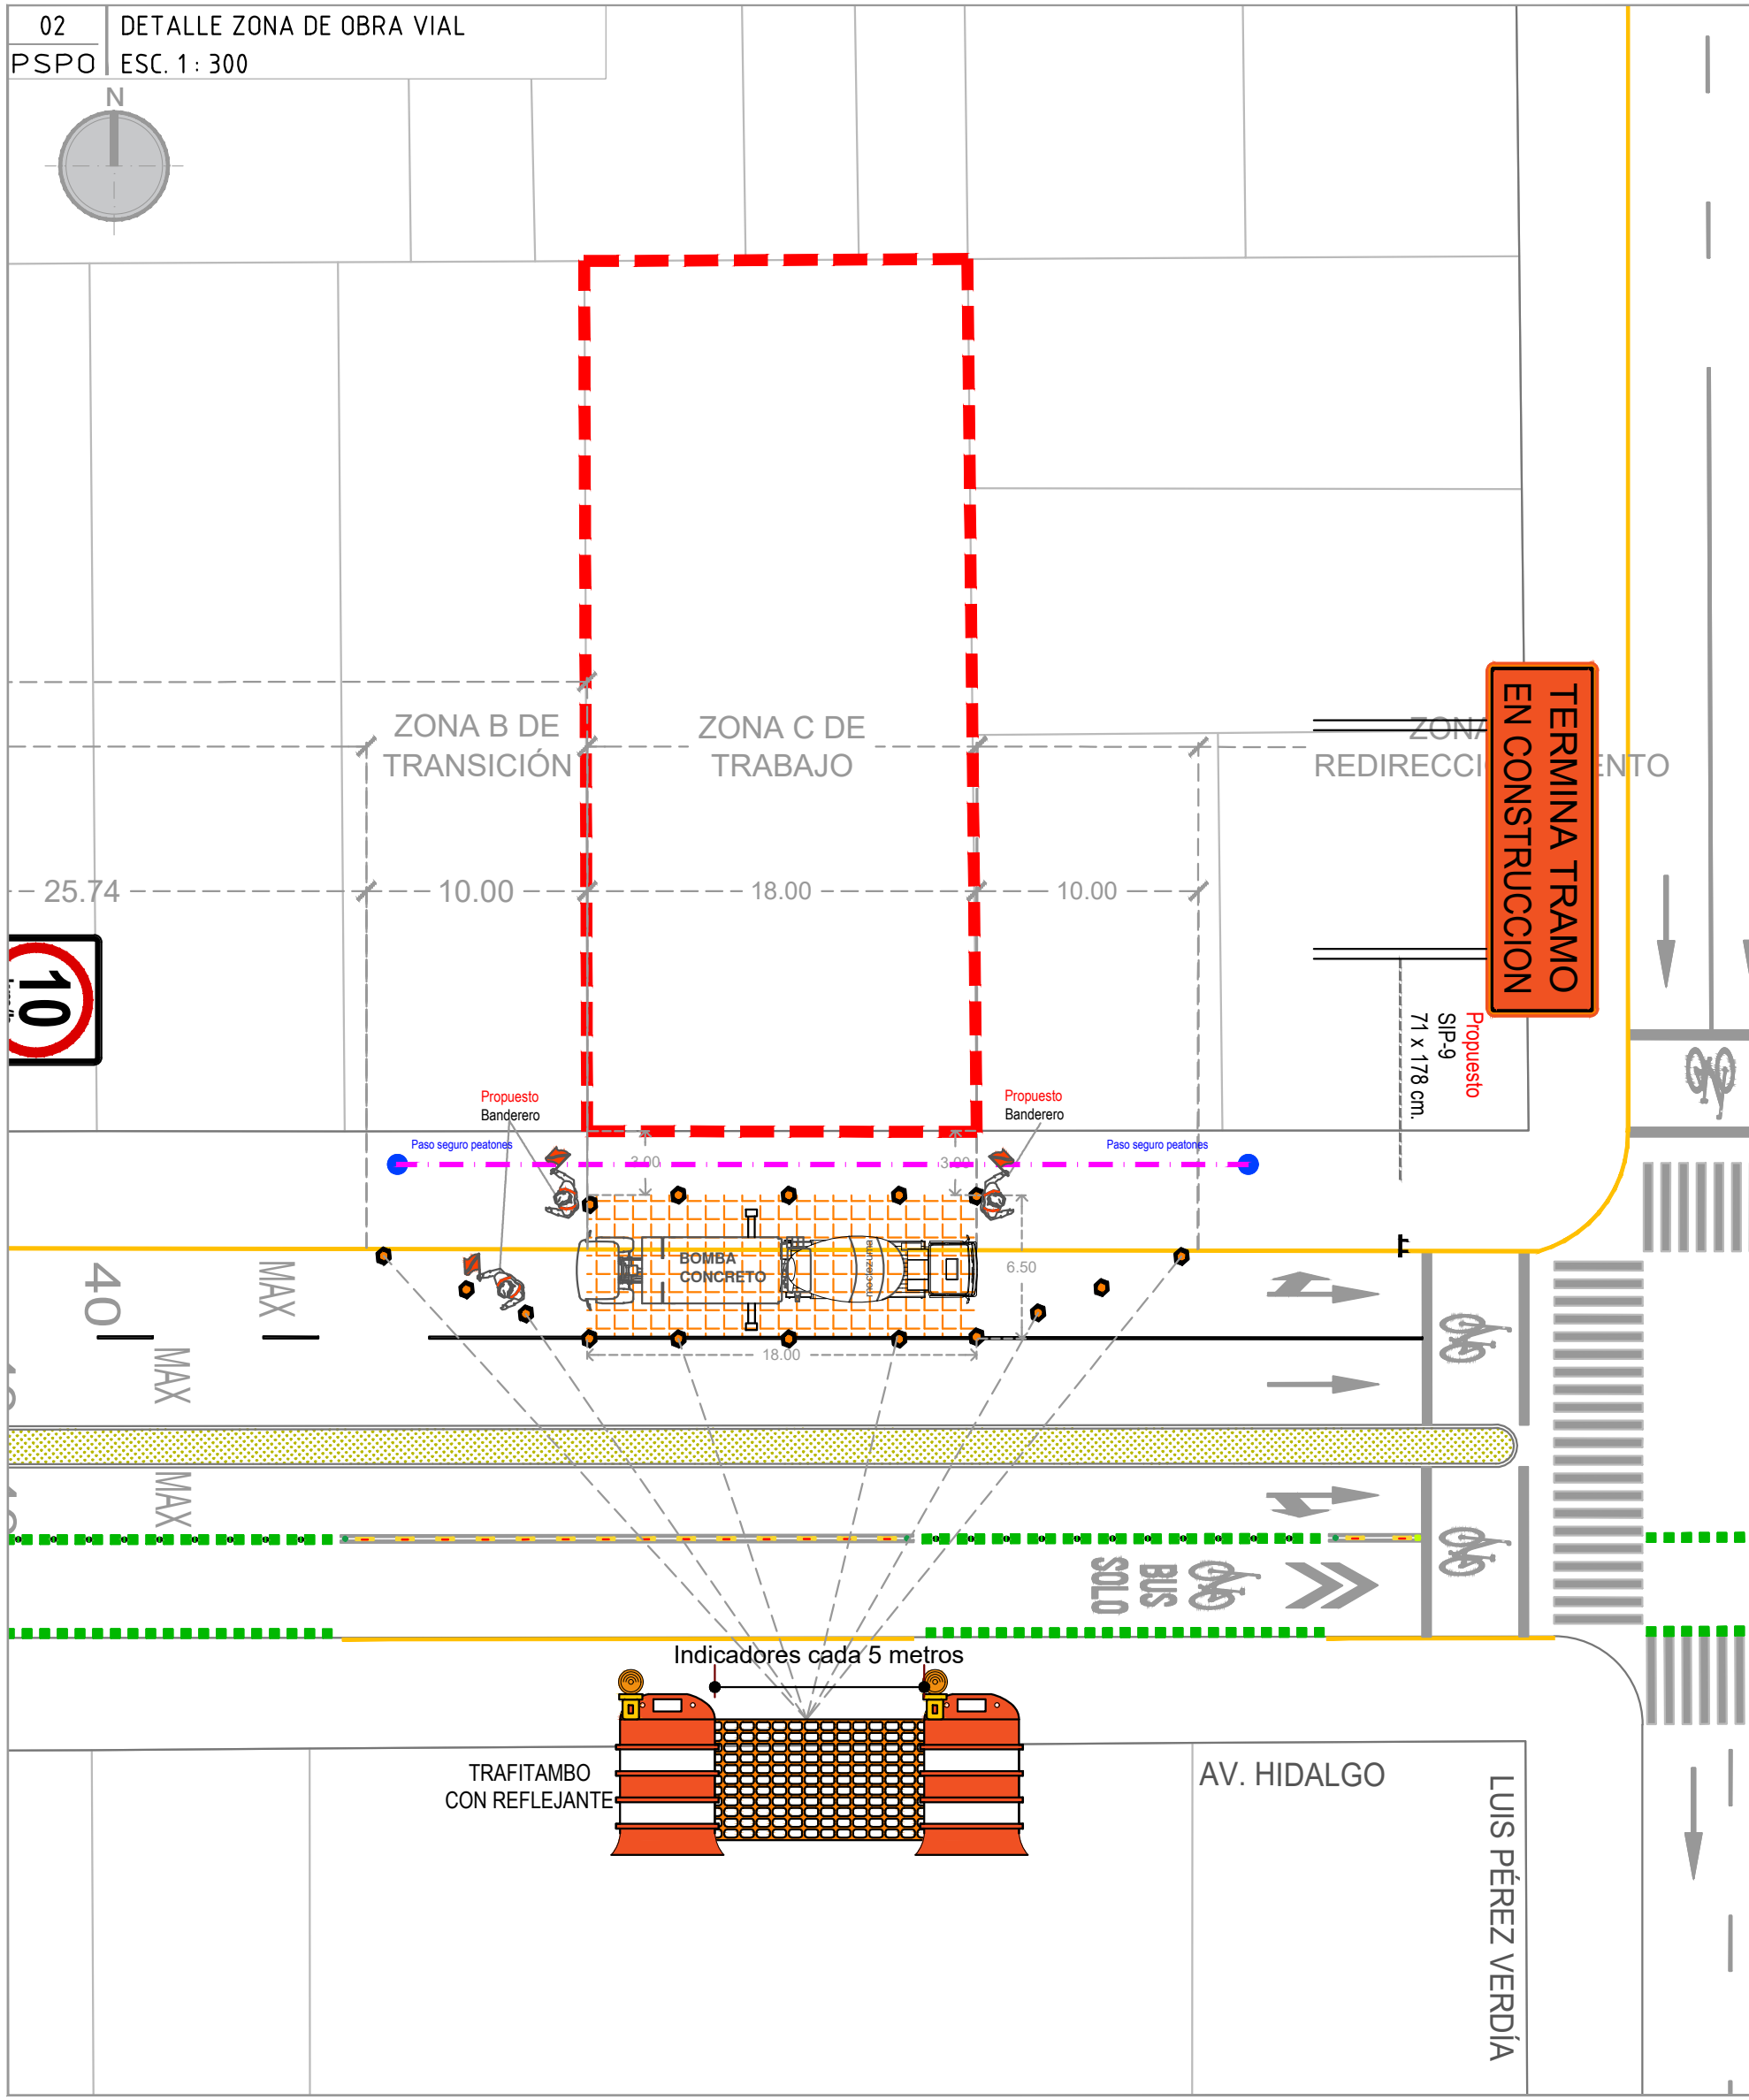


Movilidad y Transporte
Gestión Integral de la Ciudad

UBICACIÓN MACRO:

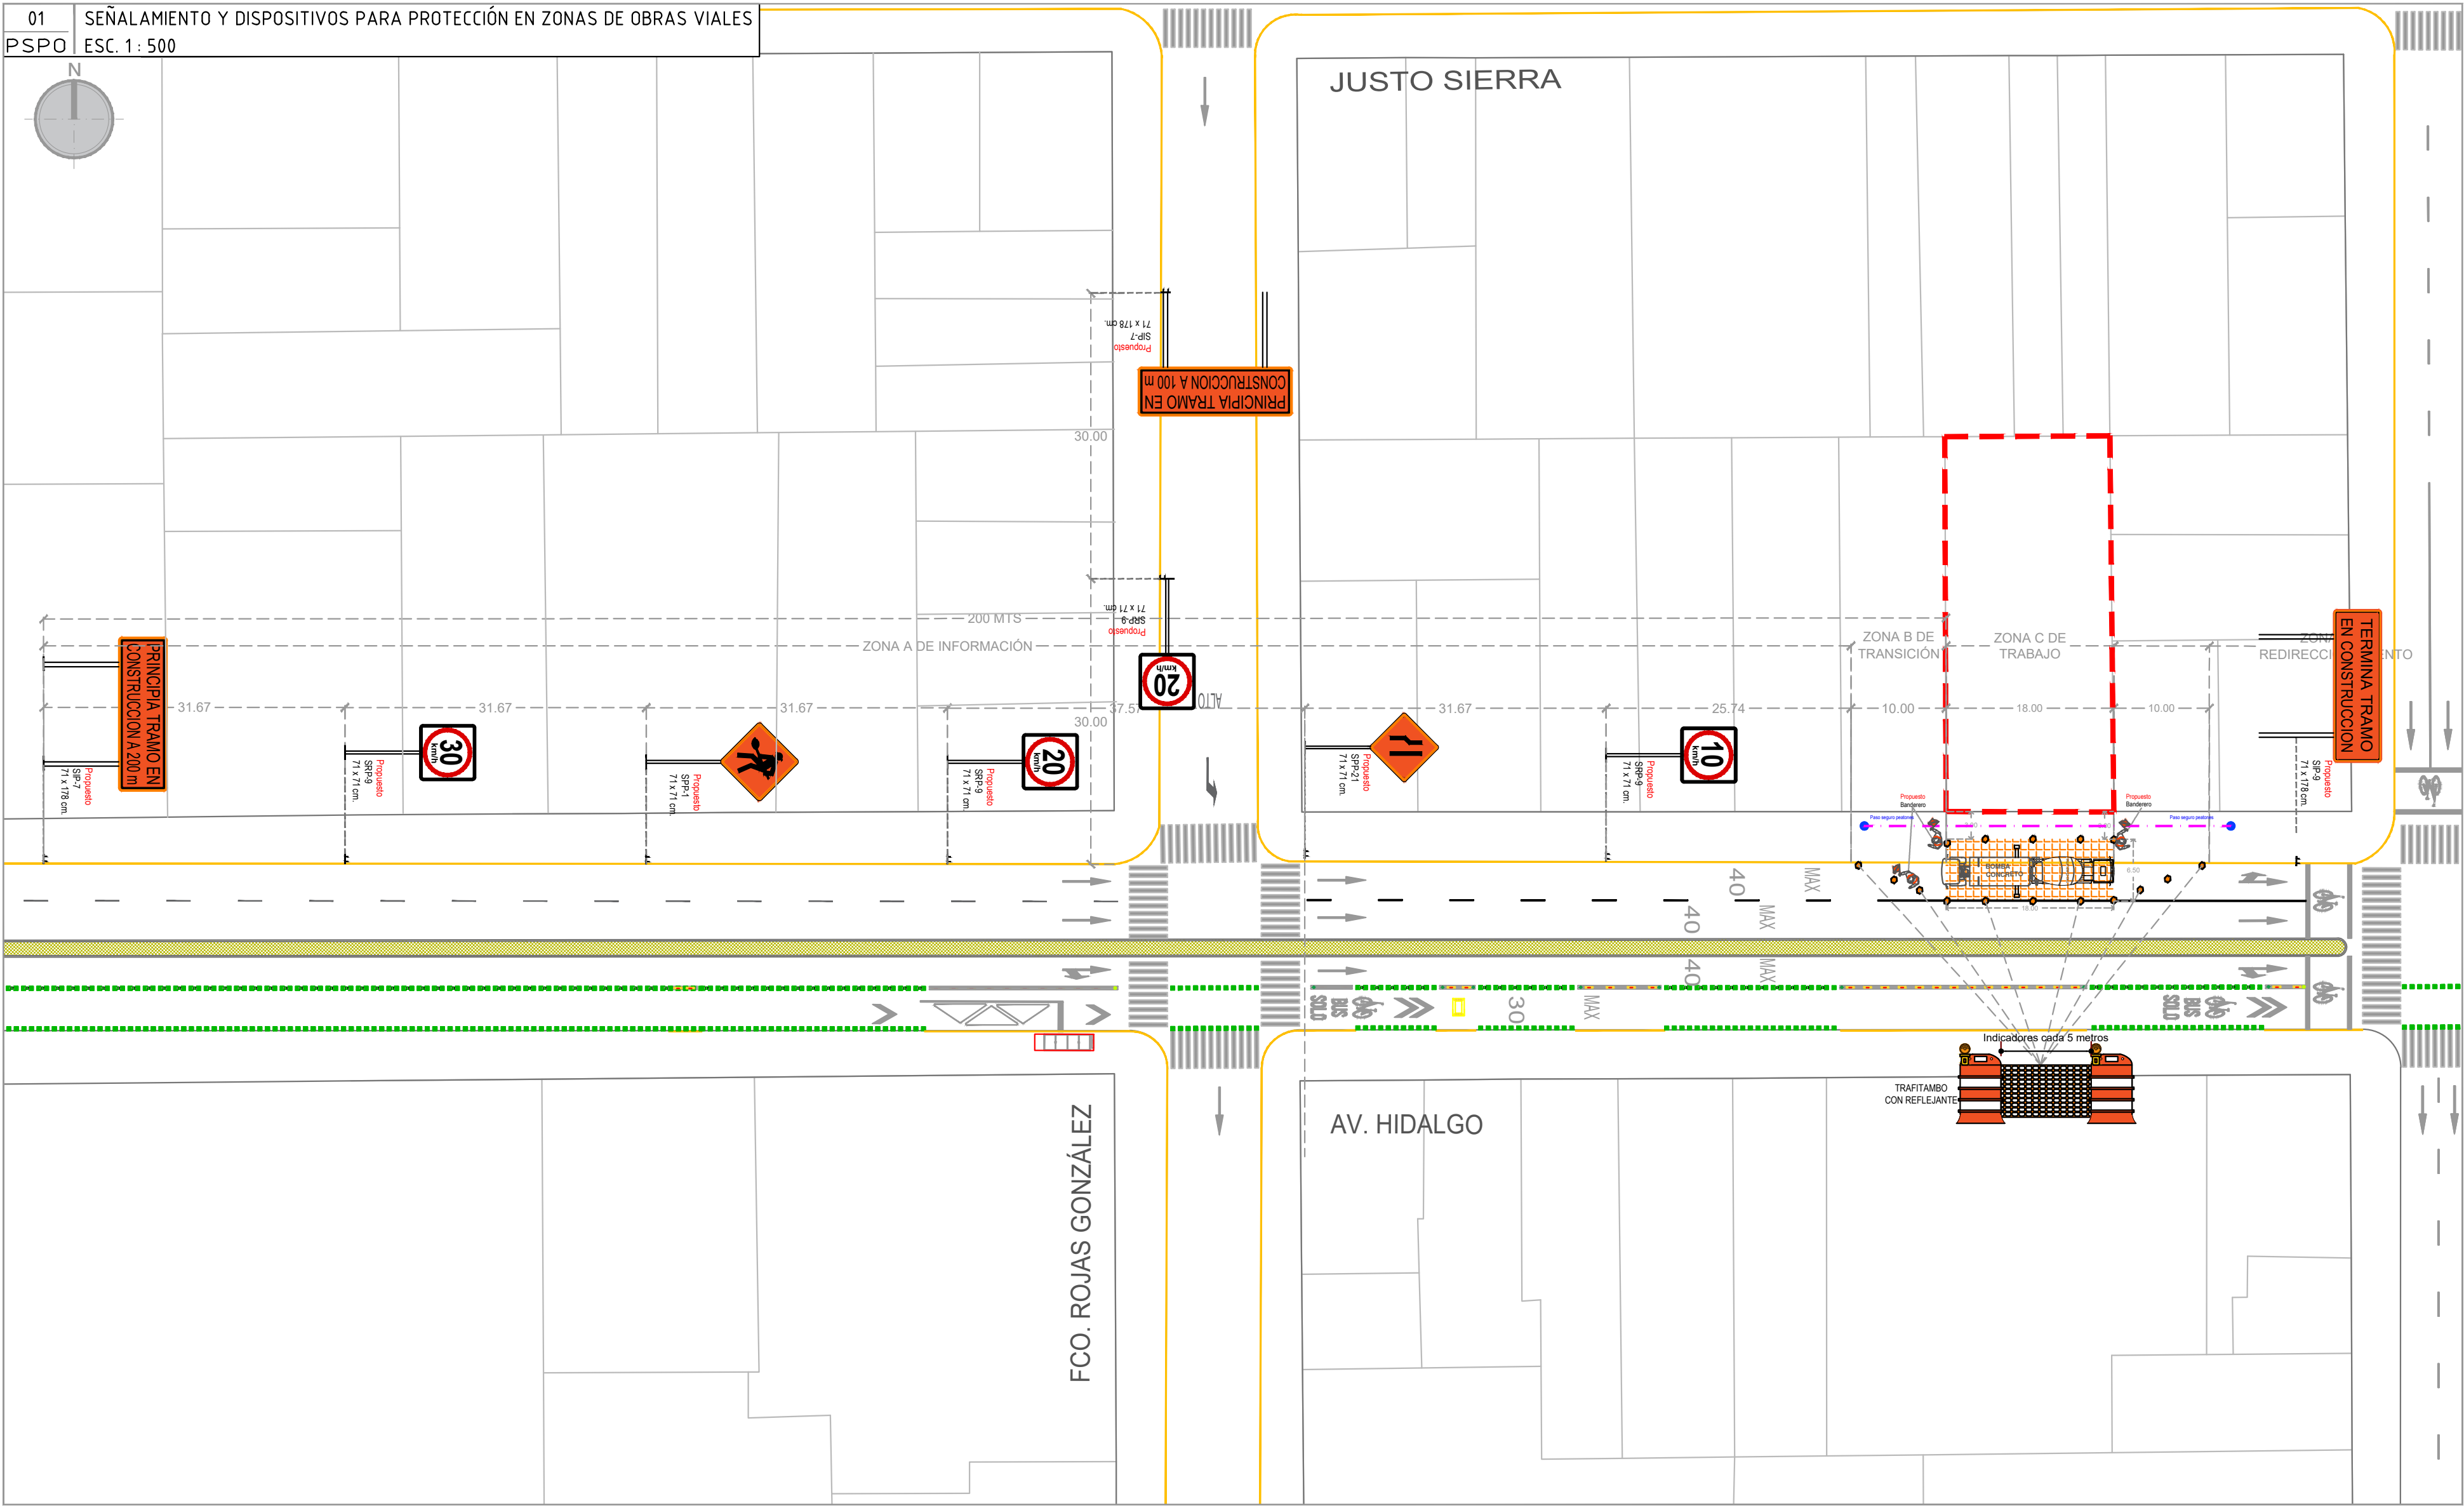

LOCALIZACIÓN MICRO:

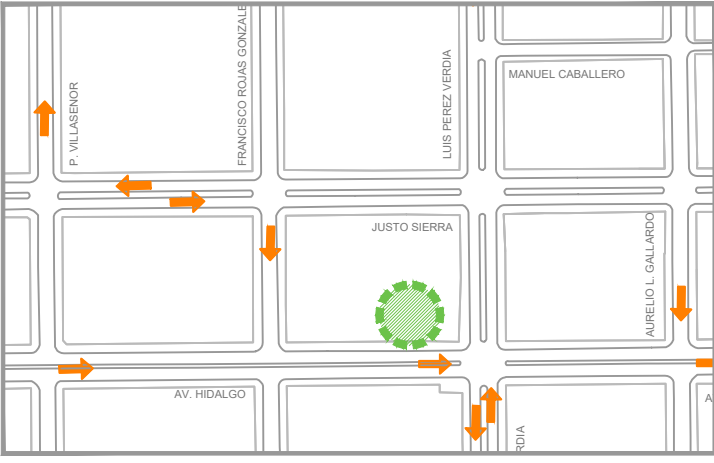

DOMICILIO:

AV. MIGUEL HIDALGO Y COSTILLA #0000

SIMBOLOGÍA:

- UBICACION OBRA - PREDIO
- ZONA DE TRABAJO OBRA
- PASO SEGURO PEATON
- SENTIDOS VIALES
- PERSONAL BANDERERO

SELLO MOVILIDAD Y TRANSPORTE DE GUADALAJARA:

NOTA: EL PRESENTE PLANO ES ÚNICAMENTE ILUSTRATIVO CON LA FINALIDAD DE ESCLARECER EL CONTENIDO MÍNIMO PARA EL TIPO DE TRÁMITE EN CUERSTIÓN POR LO QUE EL ORDEN Y DISEÑO DEL MISMO ES UN FORMATO LIBRE. ES IMPORTANTE Aclarar que LOS ALCANCES DEL MISMO SE ENCUENTRAN SUJETOS A MODIFICACIONES SEGÚN DETERMINE LA DIRECCIÓN DE MOVILIDAD Y TRANSPORTE CON BASE EN LAS CARACTERÍSTICAS DEL PROYECTO A VALIDAR.

LABORÓ:

NOMBRE Y FIRMA

NOMBRE DEL PROYECTO:
EJEMPLO DE PROYECTO
SEÑALAMIENTO Y DISPOSITIVOS
PARA PROTECCION DE OBRA VIAL

CONTENIDO DEL PLANO:

ZONA DE OBRA VIAL
CIERRE PARCIAL

ESCALA: INDICADA

FORMATO: 90X60

FECHA: AGOSTO 2024

CLAVE DEL PLANO:

PSPO-01